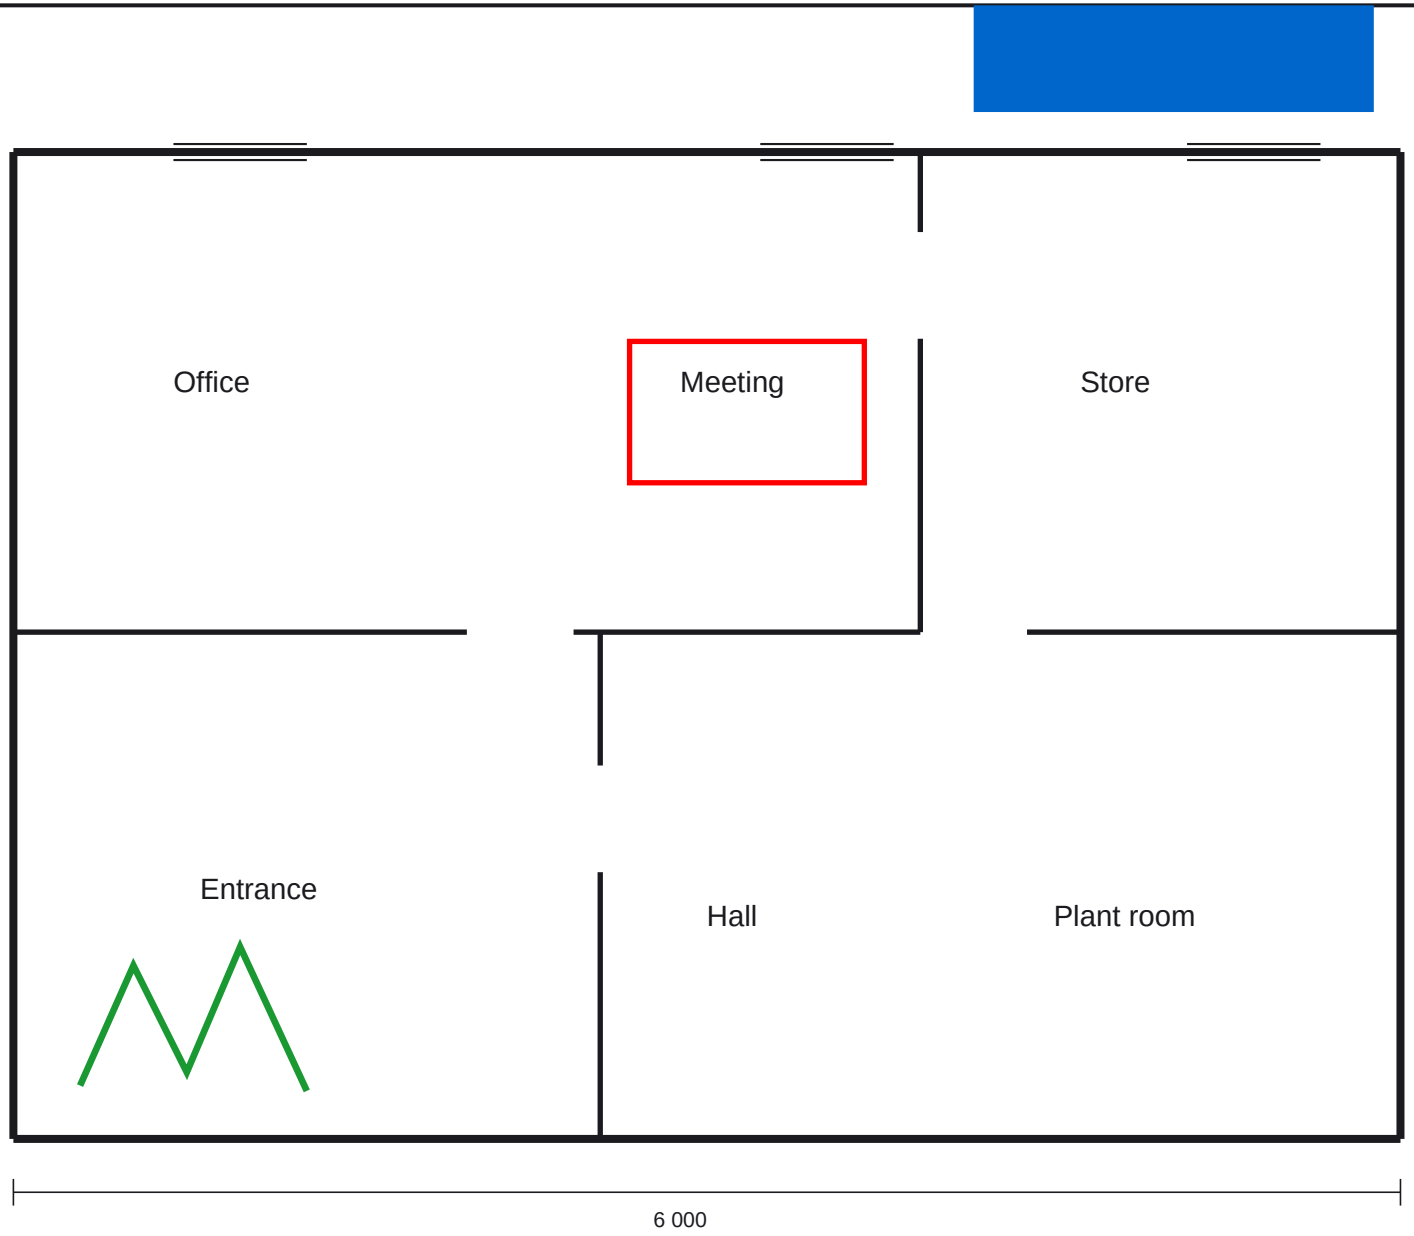

Ground floor plan

Sheet A-101 Scale 1:100 Level 0

Sample project - drawn by X-ray

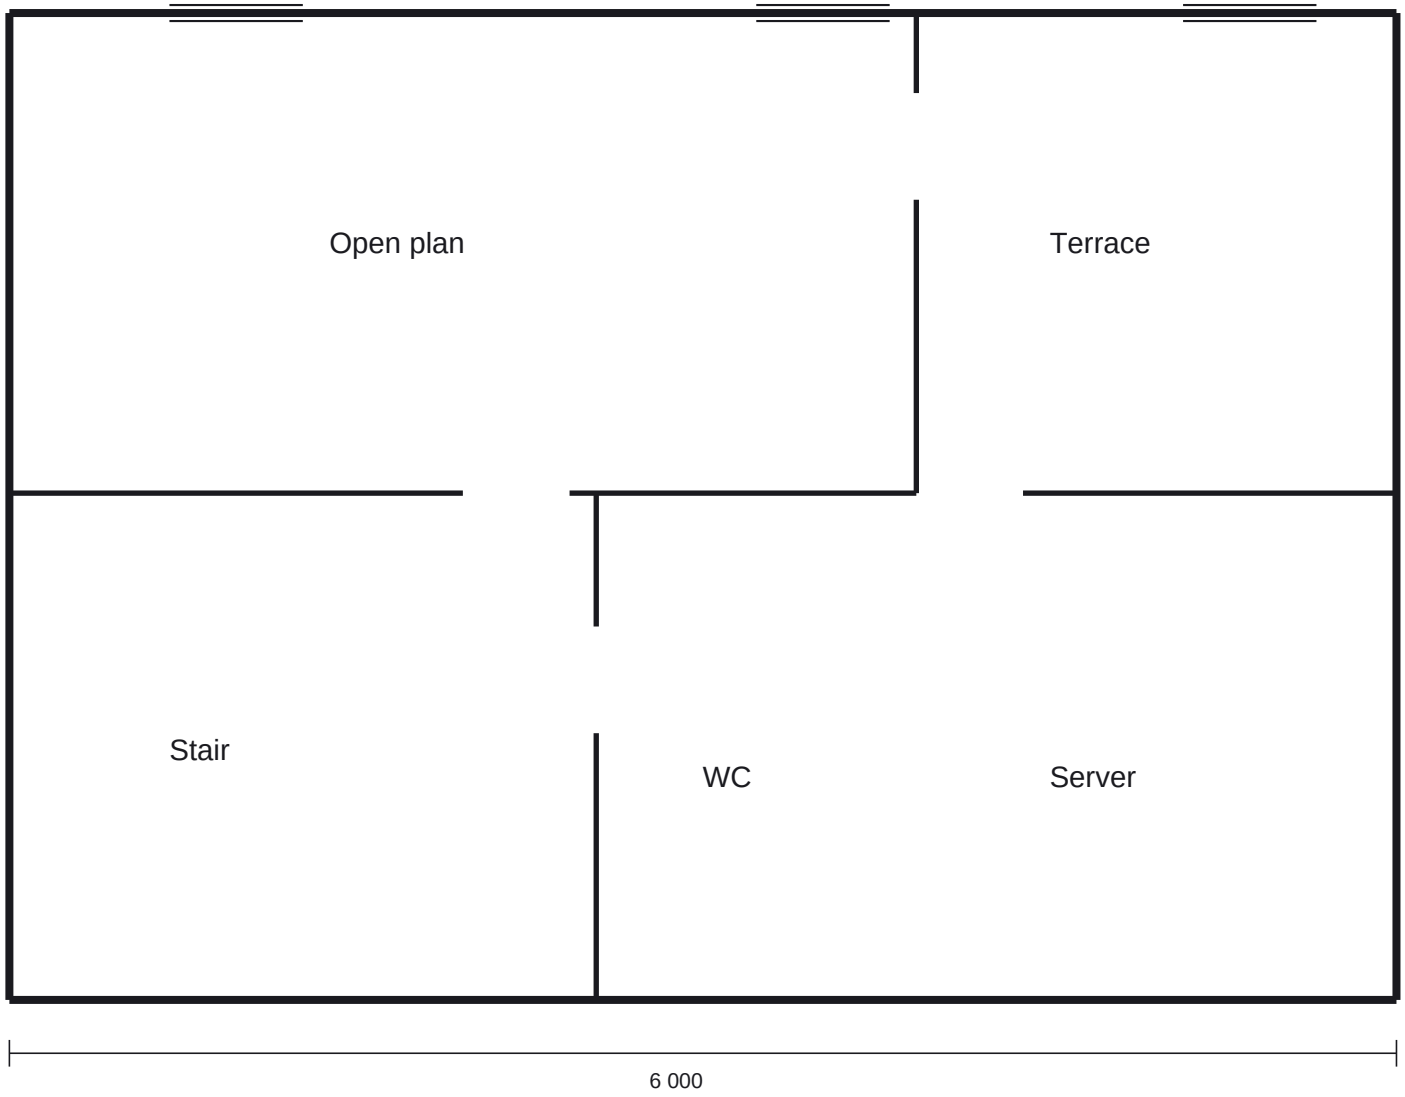

First floor plan

Sheet A-102 Scale 1:100 Level 1

Sample project - drawn by X-ray